



断面図 S=1:50

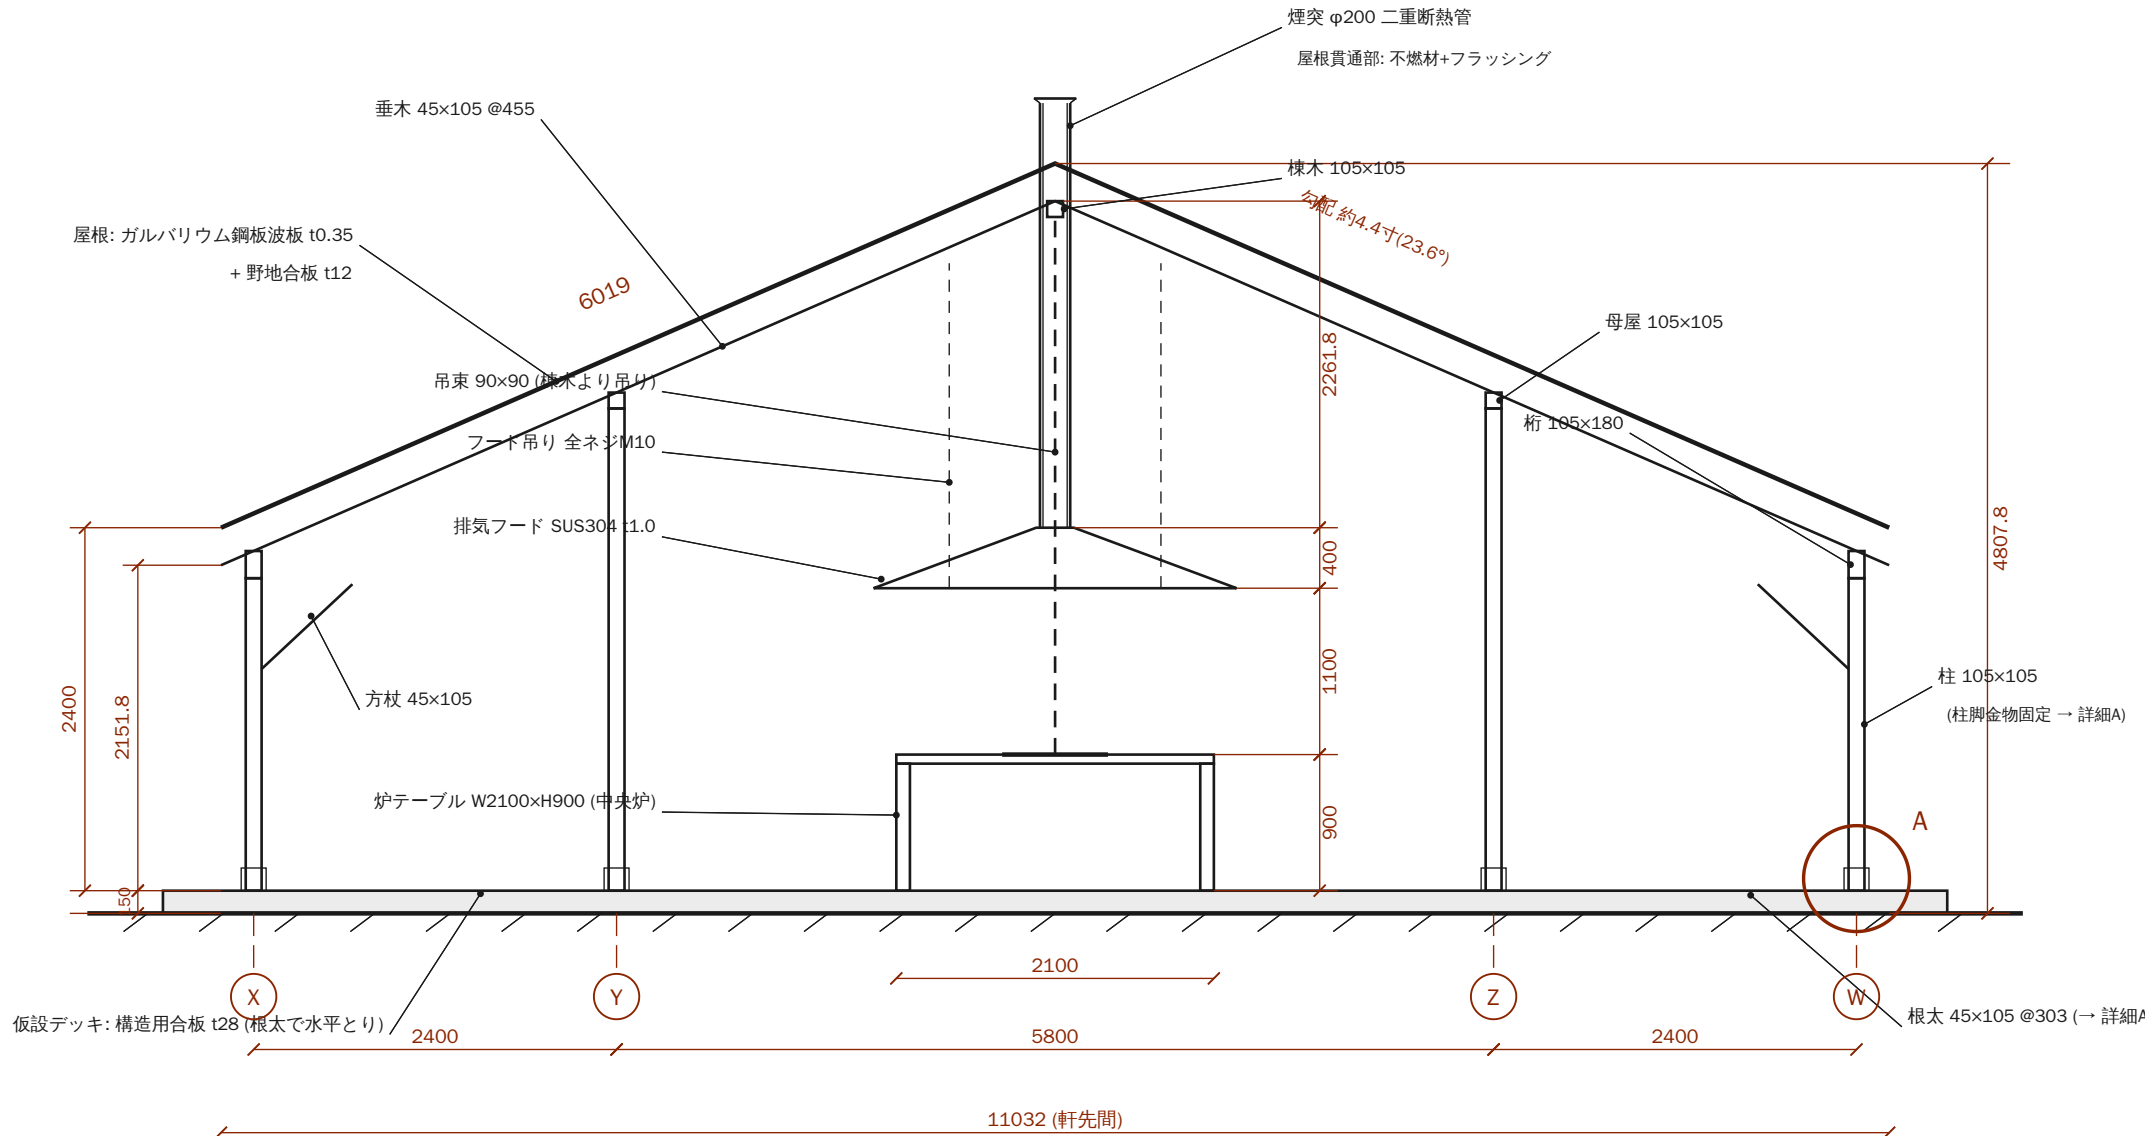

詳細A 柱脚・仮設デッキ納まり S≈1:10

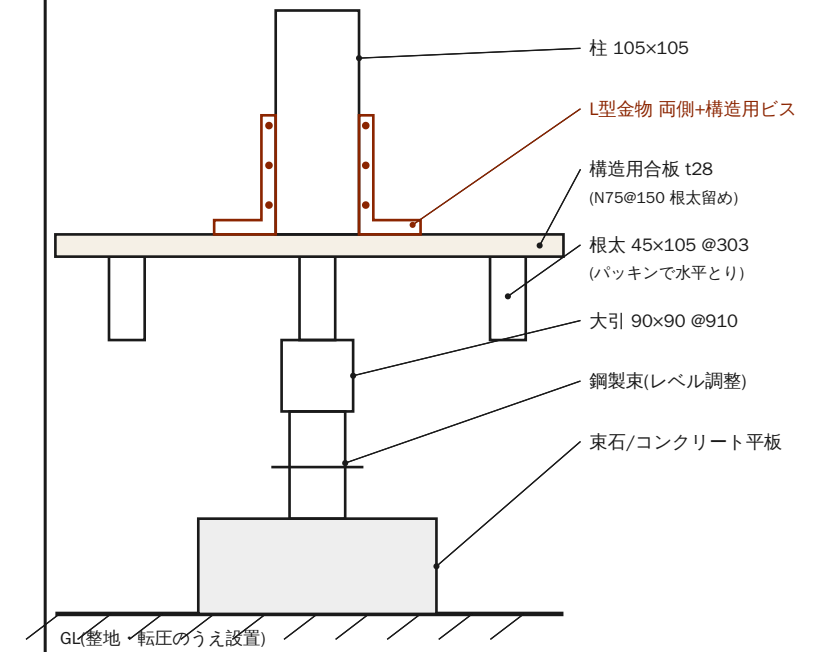

【注記・仕様(案)】

- 本図は提供断面図を基に作成した詳細図(案)。
- 部材寸法・ピッチは当社仮定値を含む。要協議。
- 仮設デッキ: 根太で水平とり、構造用合板t28敷。
- 柱は金物固定(L型金物両側+構造用ビス)。
- 屋根勾配約4.4寸・軒先間11,032・棟高GL+4,807.8。
- フード下端は炉天板+1,100(頭上クリアランス)。
- 煙突は二重断熱管φ200。屋根貫通部は不燃材(メガネ石相当)+フラッシング納めとする。
- 柱・束の配置ピッチは平面計画により決定。
- 風荷重に対する転倒・浮上り検討は別途。

有限会社 光和工業

2026.08.31 S=1:50 (A3)

東屋(仮設デッキ・炉付き) 断面詳細図(案)

